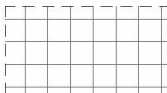
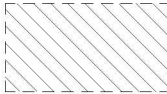
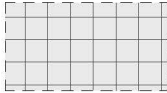


GRID NOTE:

GRIDS ARE DIMENSIONED AS TO THE BEST OVERALL POINT TO POINT DIMENSION FOR THE MOST ACCURATE FOUNDATION, BASEMENT WALL, AND MAIN WALL PLACEMENT FROM FLOOR TO FLOOR. SOME GRIDS ARE NOT DIMENSIONED FROM GRID TO GRID DUE TO THEIR NON-RELATIVE NATURE.

SHADING SYMBOL LEGEND:


-  DENOTES AREA IS OPEN TO ABOVE
-  DENOTES AREA IS OPEN TO BELOW
-  DENOTES DROPPED CLG
-  DENOTES AREA WITH OPEN OUTDOOR SPACE ABOVE

WINDOW/DOOR TAGS:

-  DENOTES WINDOW
-  DENOTES WINDOW MULLED TO WINDOW ABOVE/BELOW
-  DENOTES DOOR

WINDOW SCHEDULE		
UNIN	WIDTH	HEIGHT
1	5'-0"	3'-0"
2	3'-6"	3'-0"
100	5'-0"	6'-0"
101	5'-0"	2'-0"
102	4'-0"	6'-0"
103	2'-0"	3'-0"
104	2'-6"	3'-0"
106	4'-0"	2'-0"
200	2'-4"	3'-0"
201	2'-4"	7'-0"
202	2'-0"	3'-0"
203	2'-0"	7'-0"
204	2'-6"	6'-0"
205	6'-0"	6'-0"
206	2'-6"	2'-0"
207	2'-6"	7'-0"
208	2'-6"	2'-0"
209	4'-0"	8'-0"
210	2'-6"	4'-0"
297		

DOOR SCHEDULE			
TYPE MARK	WIDTH	HEIGHT	DESCRIPTION
1	2' - 6"	8' - 0"	
2	2' - 8"	8' - 0"	
3	2' - 6"	8' - 0"	12mm GLASS DOOR w/ CHROME HARDWARE
4	18' - 0"	8' - 0"	OVERHEAD GARAGE DOOR
5	16' - 0 1/4"	8' - 0 1/8"	4-PANEL SLIDER
6			
7	2' - 4"	8' - 0"	
16	5' - 0"	8' - 0"	
40	3' - 0"	6' - 8"	

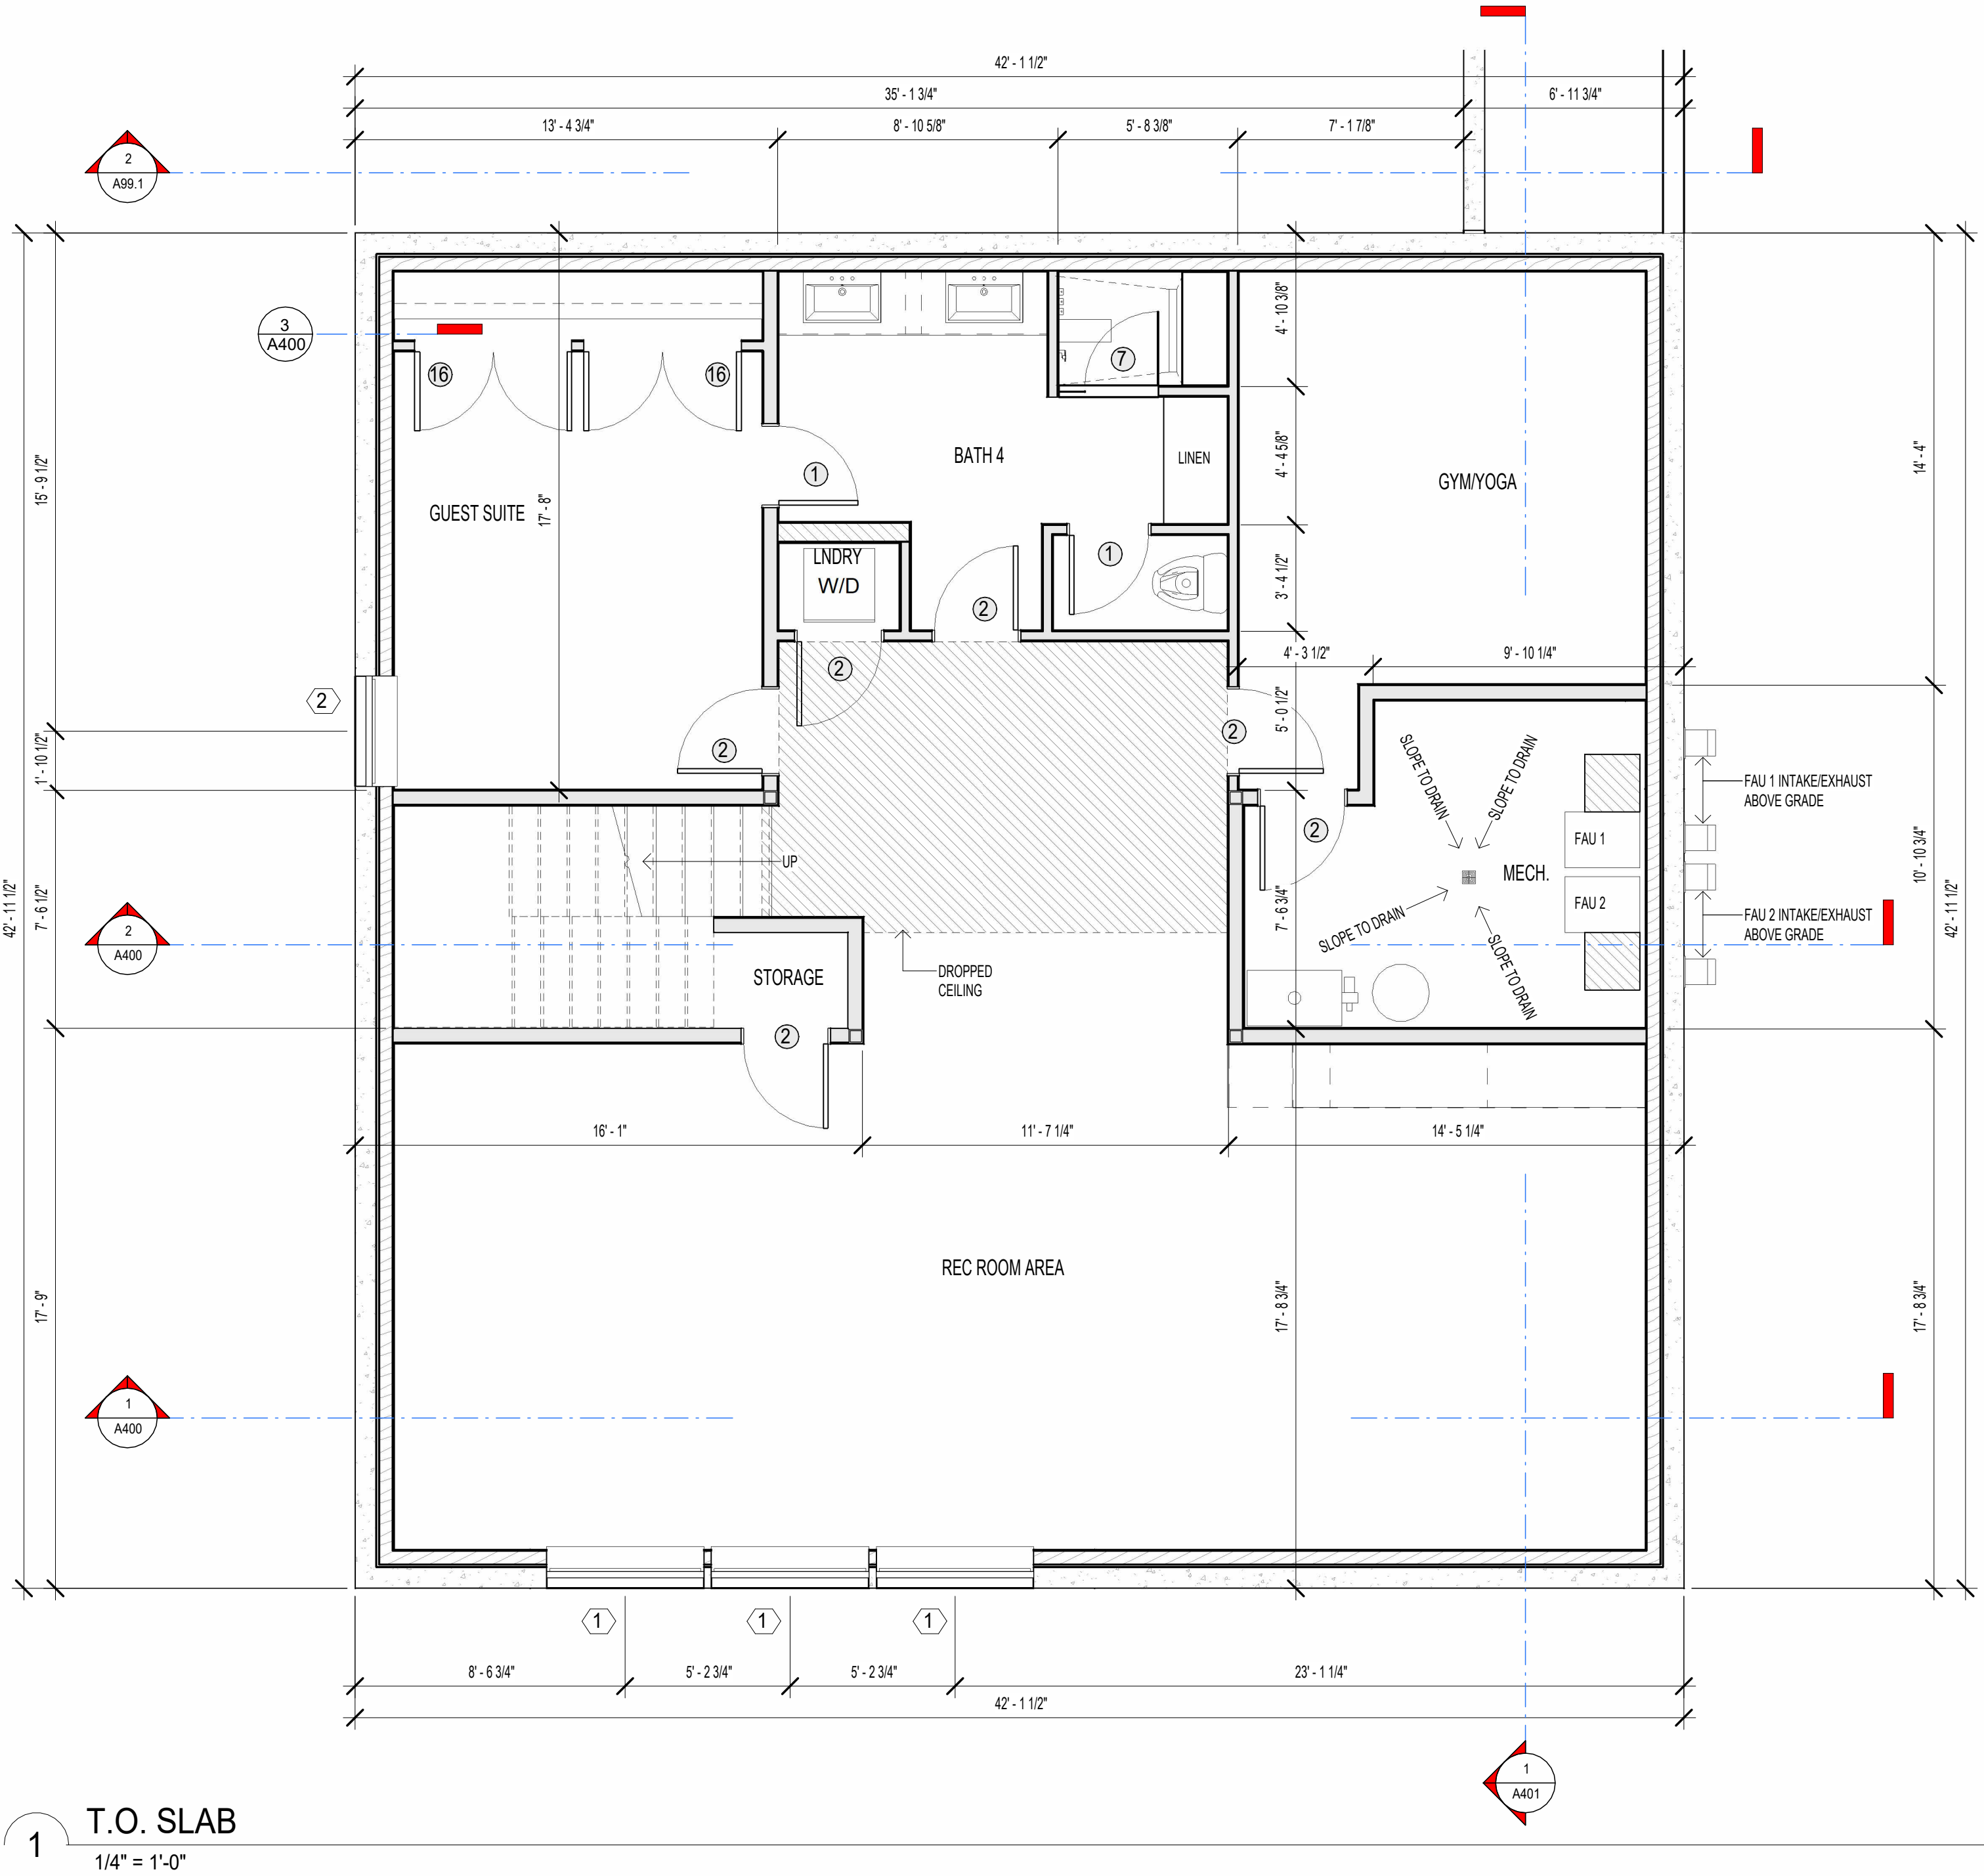

1 T.O. SLAB
1/4" = 1'-0"



DATE	5/21/25
REVISION DESCRIPTION	CONCEPTS
NO.	1
NO.	2
REVISION DESCRIPTION	DP SUBMISSION PLANS

COPYRIGHT: THESE DRAWINGS ARE THE PROPERTY OF MIDNIGHT DESIGN STUDIO, INC. ALL RIGHTS RESERVED, INCLUDING THE RIGHT OF REPRODUCTION IN WHOLE OR IN PART, IN ANY FORM, WITHOUT THE WRITTEN PERMISSION OF MIDNIGHT DESIGN STUDIO, INC. ANY COPYING OR PLAGIARIZATION WILL RESULT IN PROSECUTION.

DISCLAIMER: BUILDER SHALL REVIEW ALL DRAWINGS AND SPECIFICATIONS FOR CLARITY AND FOR ACCURACY. ALL WORK SHALL BE DONE IN A GOOD WORKMANSHIP MANNER AND TO THE BEST INDUSTRY STANDARDS AND PRACTICES, REGARDLESS OF DRAWINGS AND/OR SPECIFICATIONS. ALL DISCREPANCIES AND/OR MISTAKES SHALL BE COMMUNICATED TO MIDNIGHT DESIGN STUDIOS, INC. TO BE CORRECTED OR SUCH MISTAKES SHALL BE THE RESPONSIBILITY OF THE BUILDER/DEVELOPER/OWNER.

DATE ISSUED: 6/15/23
DESIGN BY: MJK
SCALE: 1/4" = 1'-0"

LOT 27
BLOCK 21
PLAN 3057HP
14 LISSINGTON DR SW
CALGARY, AB

A100

BASEMENT FLOOR PLAN

ISSUED FOR ENG.

MIDNIGHT DESIGN STUDIO, INC.
5319 3RD STREET SE, CALGARY
(403)815-0604
www.midnightdesignstudio.ca

BOXHAUS

TOTAL BASEMENT DEVELOPMENT - 1,556 SQ. FT.
MAIN FLOOR AREA - 1,911 SQ. FT.
UPPER FLOOR AREA - 1,818 SQ. FT.
TOTAL AREA - 3,729 SQ. FT.