


GRIDS ARE DIMENSIONED AS TO THE BEST OVERALL POINT TO POINT DIMENSION FOR THE MOST ACCURATE FOUNDATION, BASEMENT WALL, AND MAIN WALL PLACEMENT FROM FLOOR TO FLOOR. SOME GRIDS ARE NOT DIMENSIONED FROM GRID TO GRID DUE TO THEIR NON-RELATIVE NATURE.



DENOTES AREA IS OPEN TO ABOVE



DENOTES WINDOW

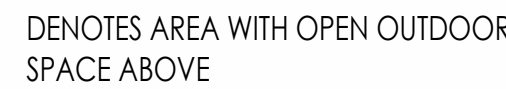

DOOR SCHEDULE			
TYPE MARK	WIDTH	HEIGHT	DESCRIPTION
1	2'- 6"	8'- 0"	12mm GLASS DOOR w/ CHROME HARDWARE OVERHEAD GARAGE DOOR 4-PANEL SLIDER
2	2'- 8"	8'- 0"	
3	2'- 6"	8'- 0"	
4	18'- 0"	8'- 0"	
5	16'- 0 1/4"	8'- 0 1/8"	
6			
7	2'- 4"	8'- 0"	
16	5'- 0"	8'- 0"	
40	3'- 0"	6'- 8"	

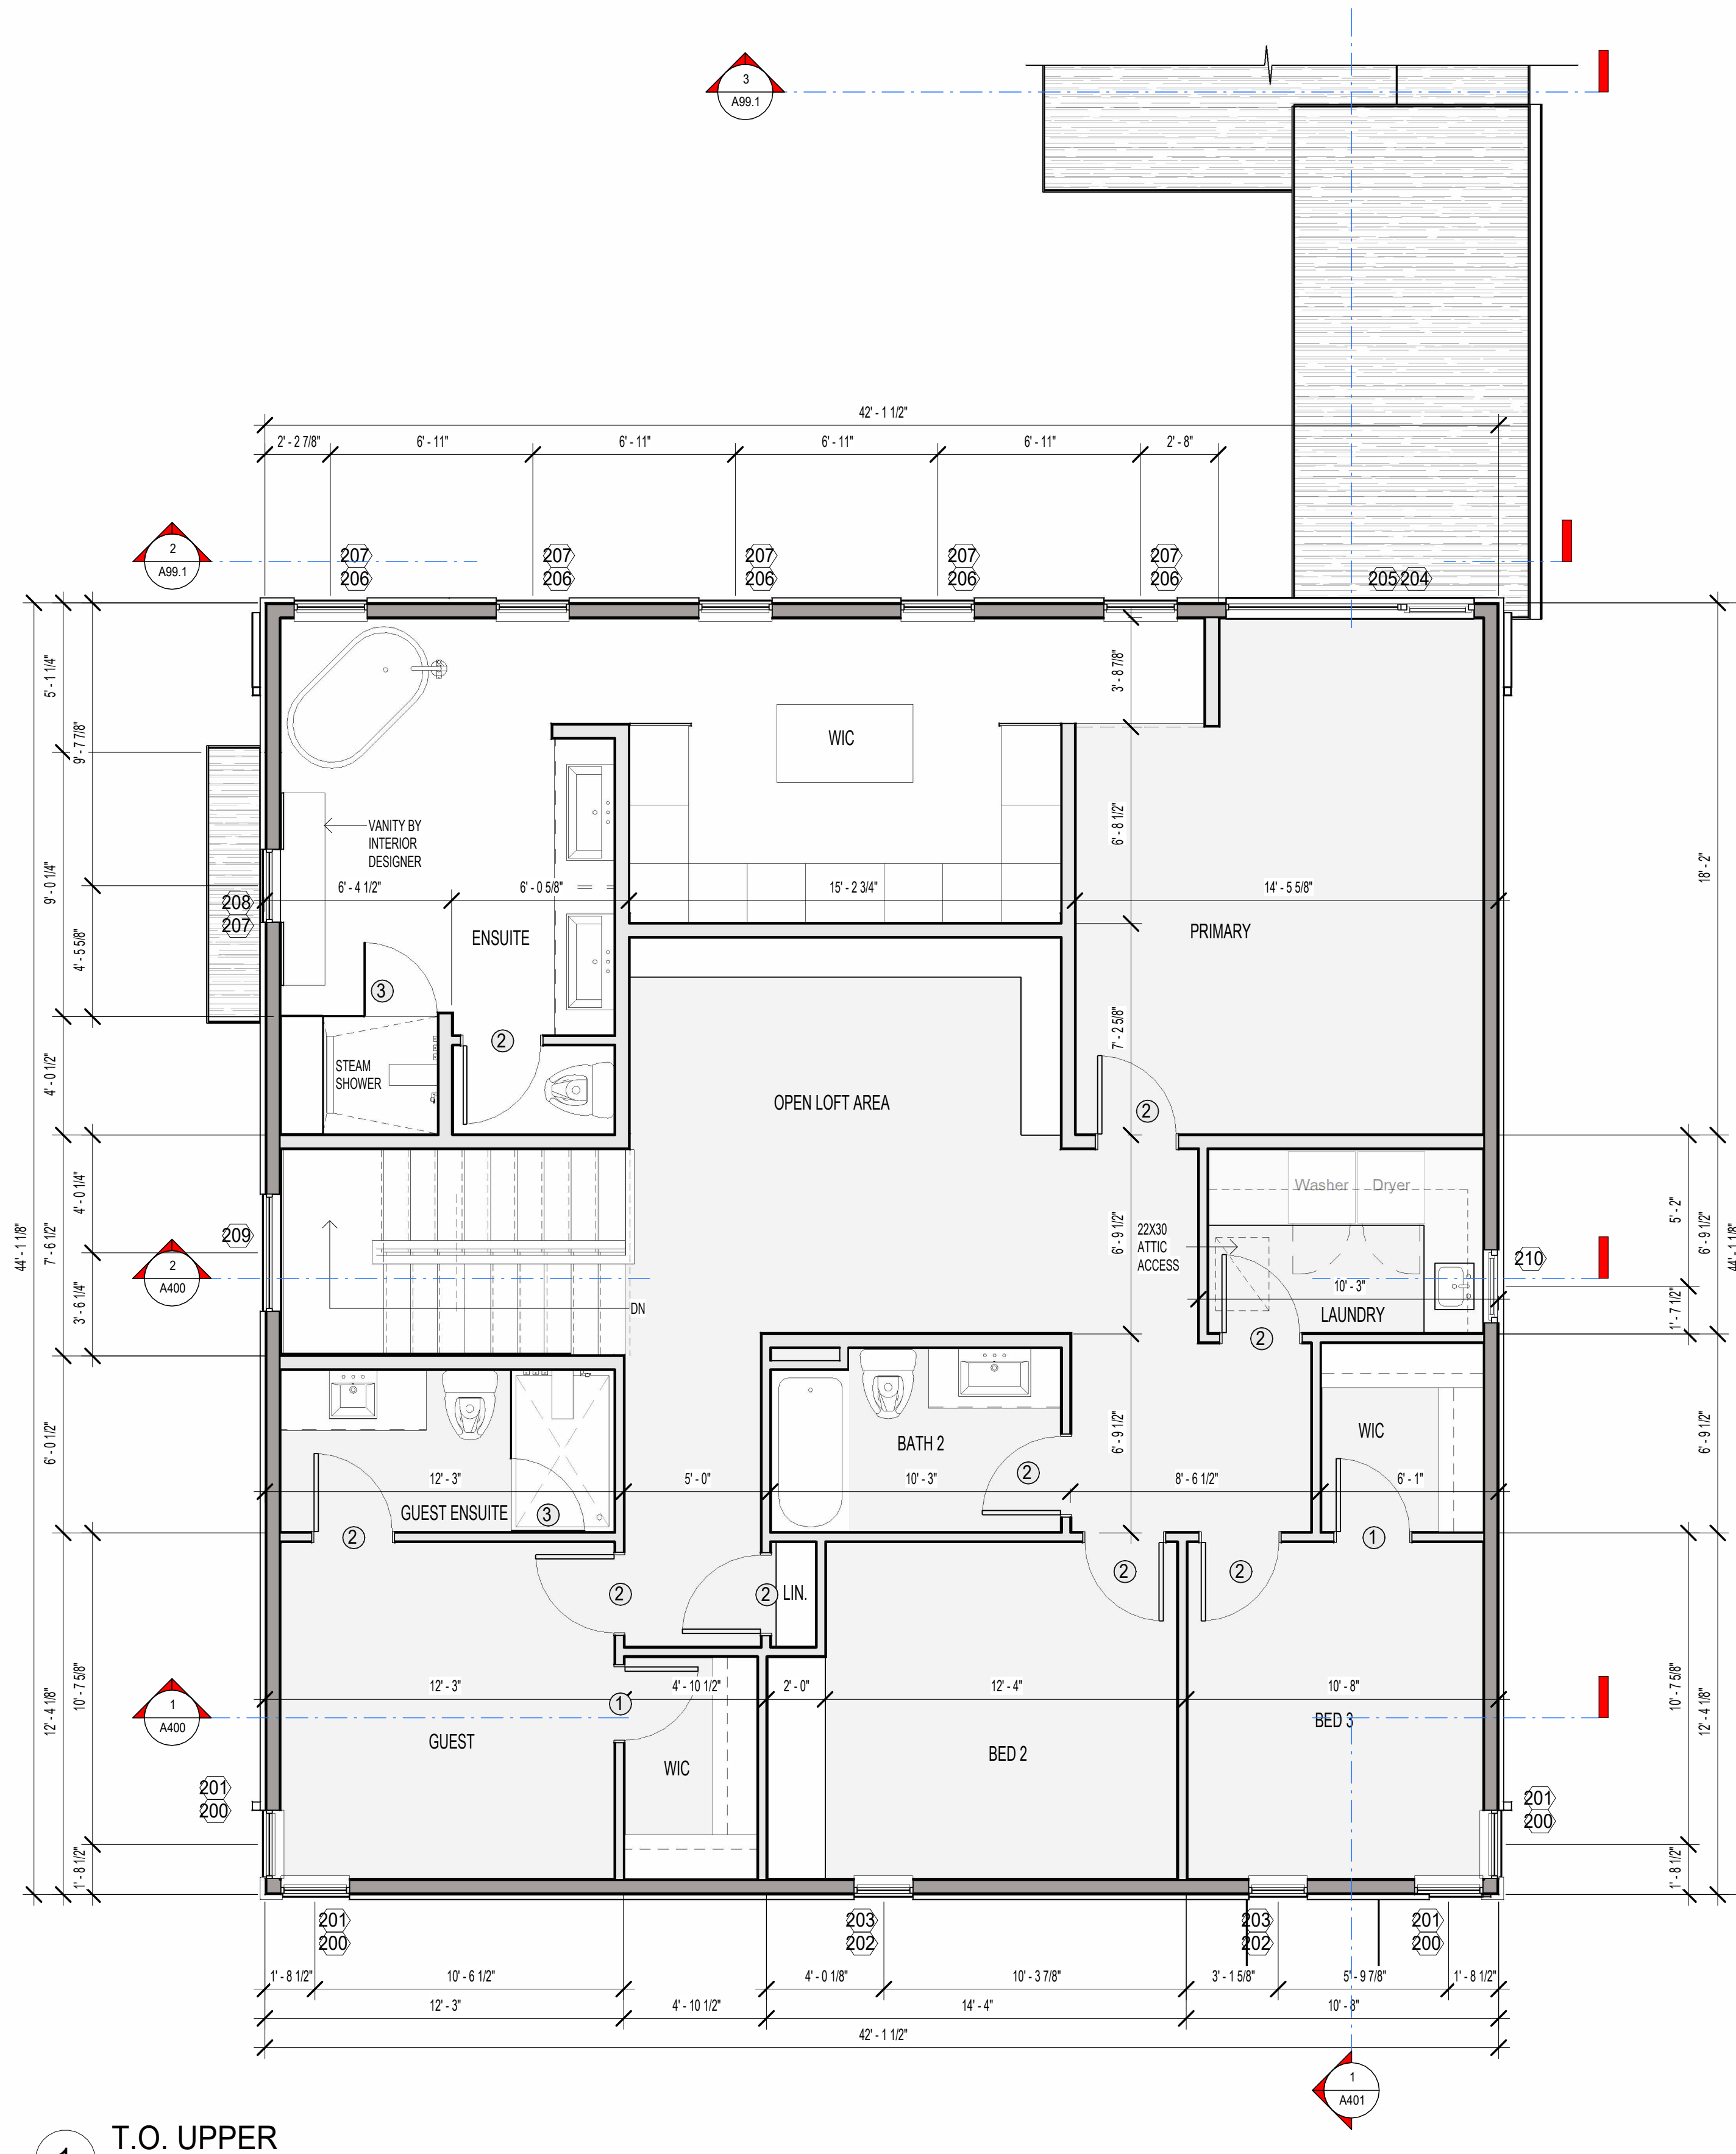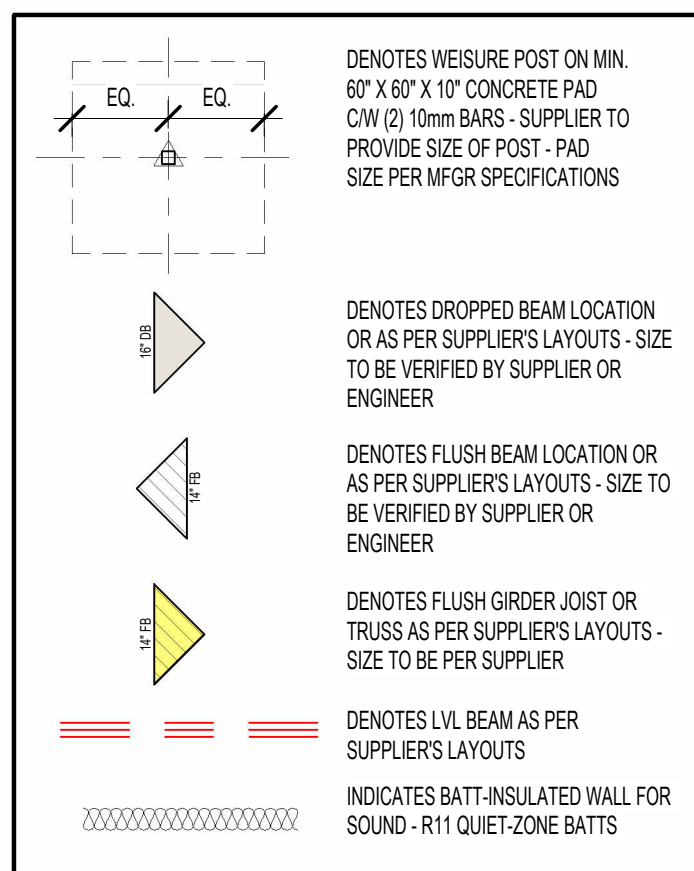

1 T.O. UPPER
1/4" = 1'-0"

NO.		REVISION DESCRIPTION	DATE
1		CONCEPTS	5/21/25
2		DP SUBMISSION PLANS	7/12/25

COPYRIGHT:
 THESE DRAWINGS ARE THE PROPERTY OF MIDNIGHT DESIGN STUDIO, INC. ALL RIGHTS RESERVED, INCLUDING THE RIGHT OF REPRODUCTION IN WHOLE OR IN PART, IN ANY FORM, WITHOUT THE WRITTEN PERMISSION OF MIDNIGHT DESIGN STUDIO, INC. ANY COPYING OR PLERAZIGATION WILL RESULT IN PROSECUTION.

DISCLAIMER:
 BUILDER SHALL REVIEW ALL DRAWINGS AND SPECIFICATIONS FOR CLARITY AND FOR ACCURACY. ALL WORK SHALL BE DONE IN A GOOD WORKMANSHIP MANNER AND TO THE BEST INDUSTRY STANDARDS AND PRACTICES, REGARDLESS OF DRAWINGS AND/OR SPECIFICATIONS. ALL DISCREPANCIES AND/OR MISTAKES SHALL BE COMMUNICATED TO MIDNIGHT DESIGN STUDIOS, INC. TO BE CORRECTED OR SUCH MISTAKES SHALL BE THE RESPONSIBILITY OF THE BUILDER/DEVELOPER/OWNER.

DATE ISSUED:	6/15/23
DESIGN BY:	Designer
SCALE:	1/4" = 1'-0"

LOT 27
 BLOCK 21
 PLAN 3057HP
 14 LISSINGTON DR SW
 CALGARY, AB

A102

UPPER FLOOR PLAN
ISSUED FOR ENG.
MIDNIGHT DESIGN STUDIO, INC. 5319 3RD STREET SE, CALGARY (403)815-0604 www.midnightdesignstudio.ca

BOXHAUS

TOTAL BASEMENT DEVELOPMENT -	1,556 SQ. FT.
MAIN FLOOR AREA -	1,911 SQ. FT.
UPPER FLOOR AREA -	<u>1,818 SQ. FT.</u>
TOTAL AREA - 3,729 SQ. FT.	